



THE PLEDGE... Nov 2019

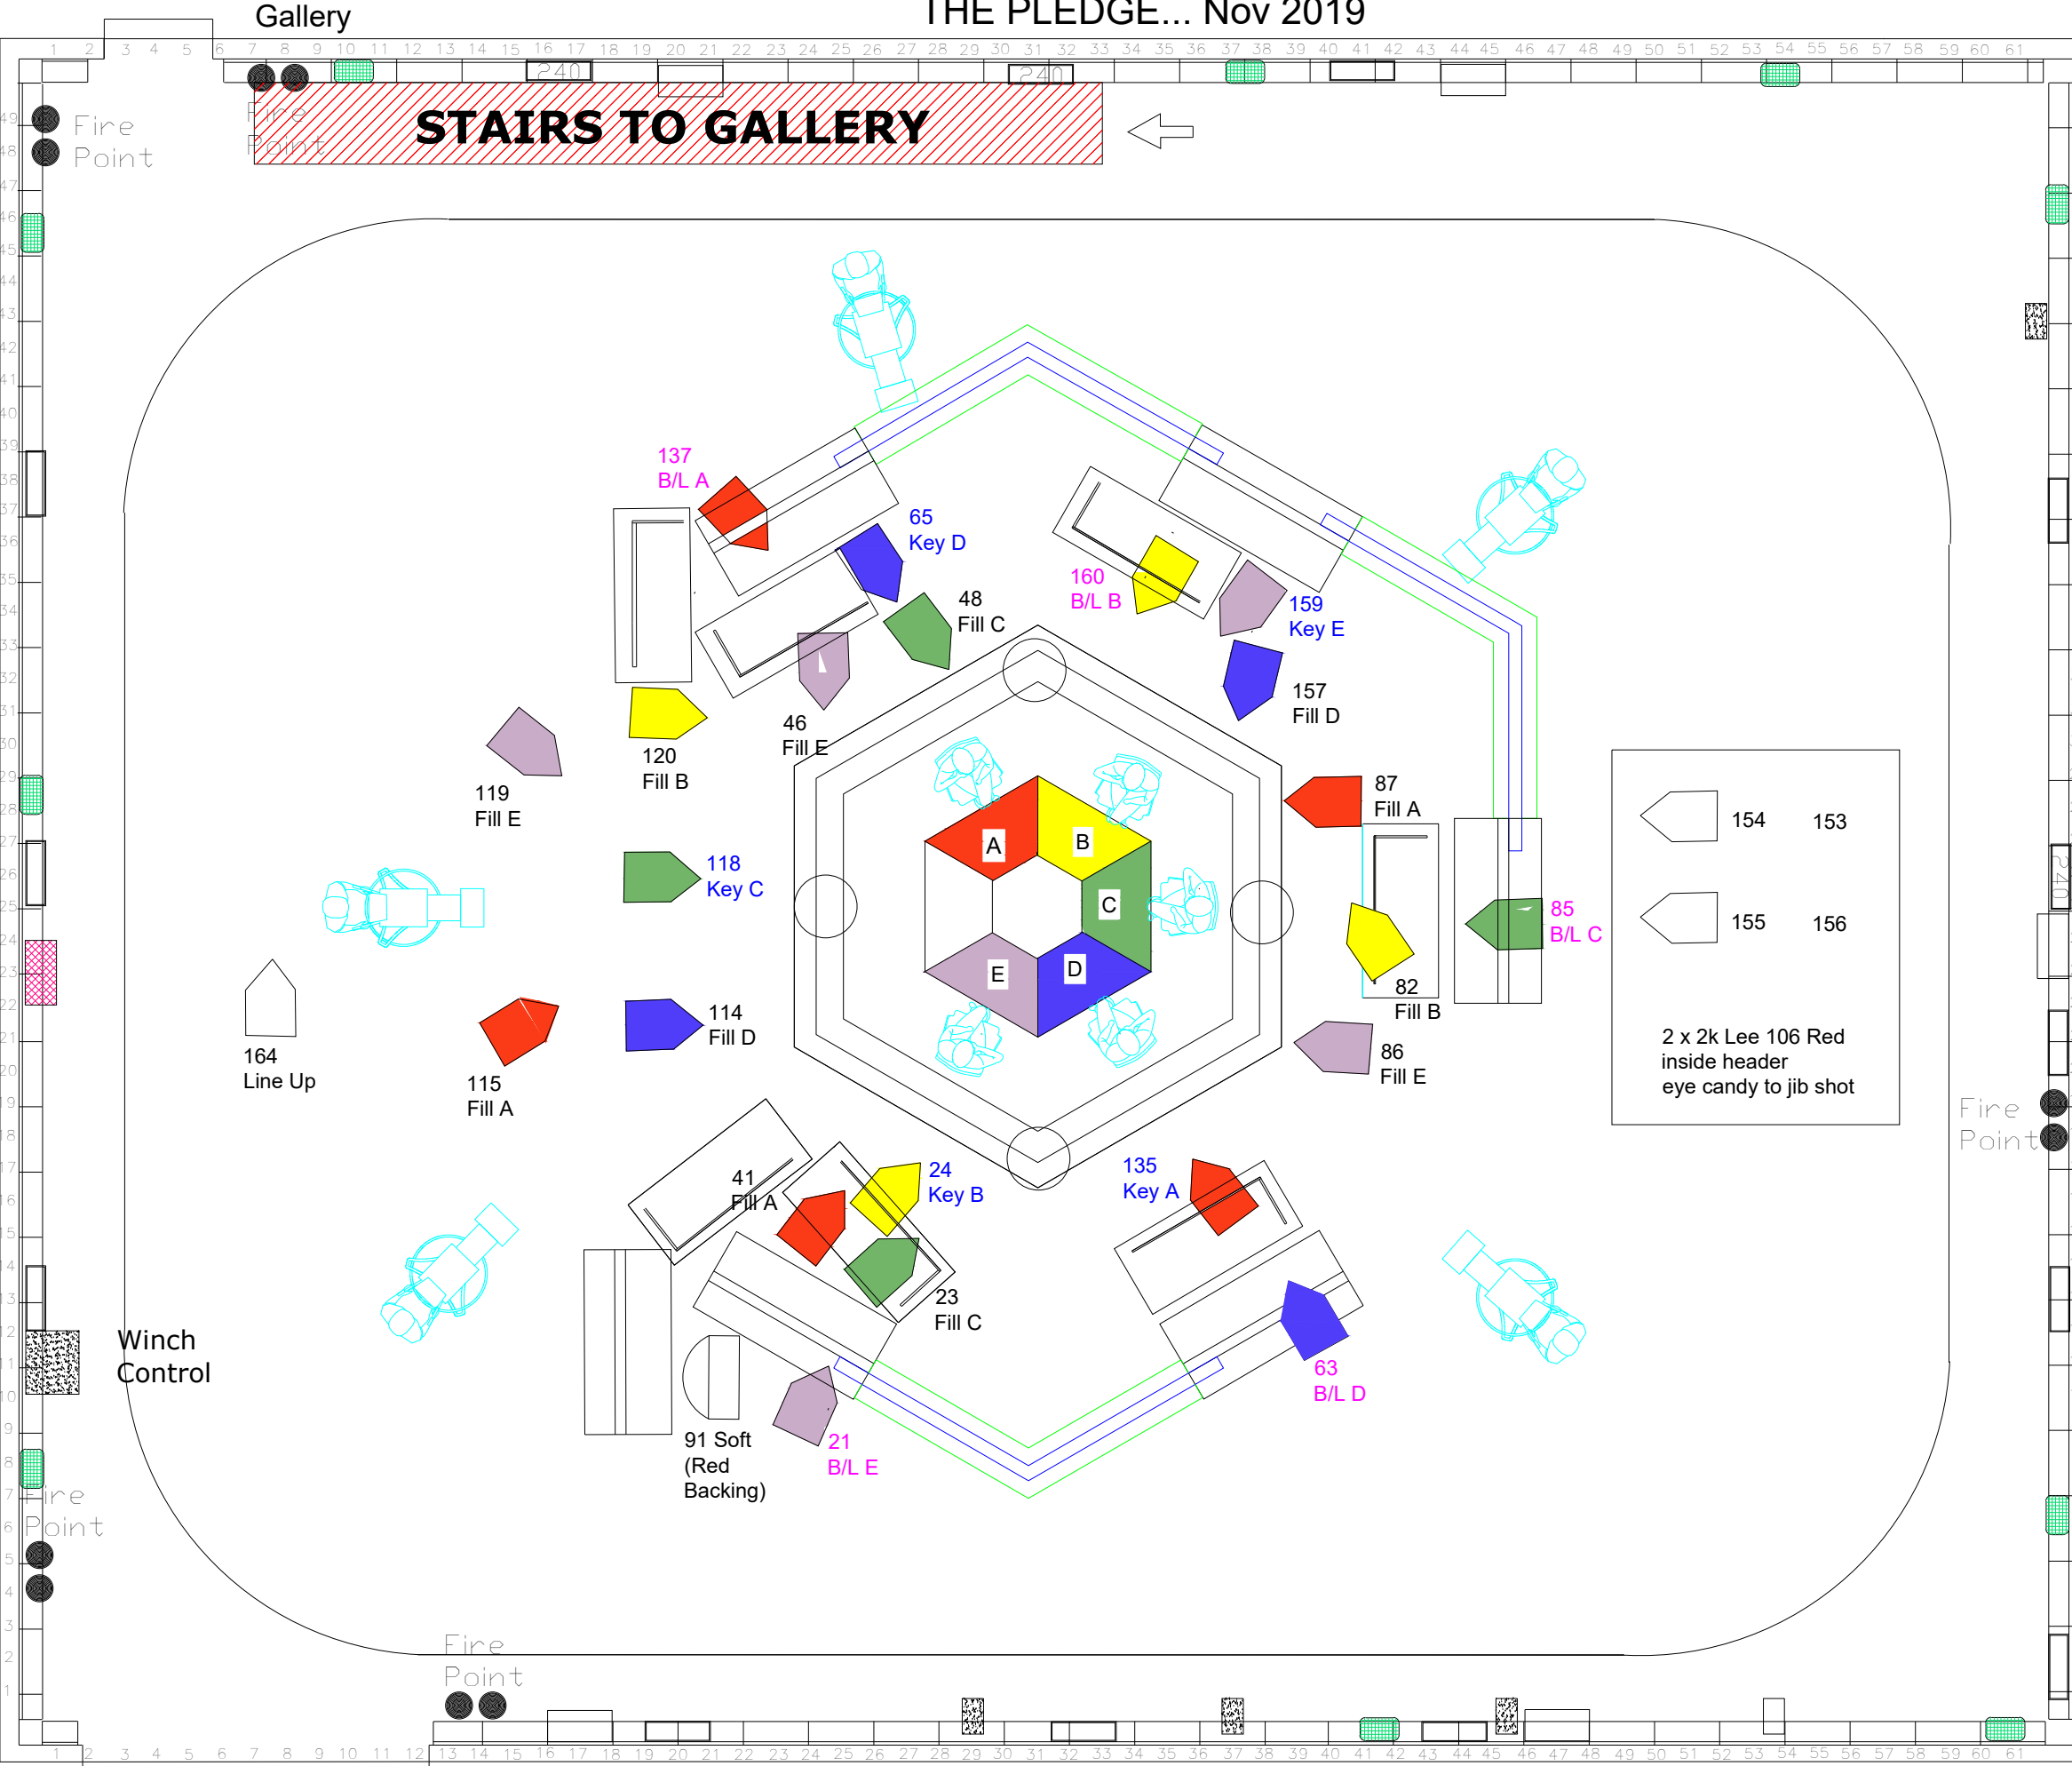

Lighting Table						
	A	B	C	D	E	Groups
KEY	135	24	118	65	159	107
Cam Left	41	120	48	157	86	108
Cam Right	87	82	23	114	46	
B/L	137	160	85	63	21	109
Frontal	115				119	

GEL	
Key Lights = $\frac{1}{4}$ CTO	2x Side Wrap
Fill/Kickers = F1	2x Side Wrap
Back Lights = $\frac{1}{2}$ CTB	Top Wrap

LED channels	
501 = Header	
502 = Rostrum	
503 = Rostrum down light	
504 = Desk Fins	
505 = Desk down light	
511 = P	
521 = P	
522 = L	
523 = E	
524 = D	
525 = G	
526 = E	
531 = Rail	
532 = Rail	
533 = Rail	
534 = Rail	
541 = Floating Pledge	
542 Acrylic Logos inside set area	

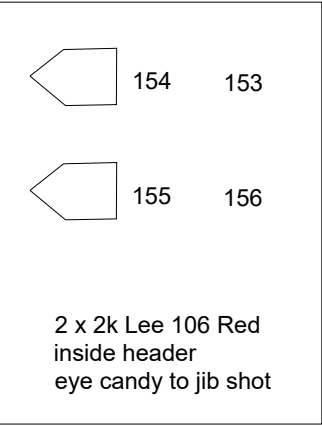

<--scene dock

Lights Raw Mains Wall Box Safety Lights 13A 13 Amp Winches

The Pledge 2019 v13	
Studio	Date 07.11.2019
F	